


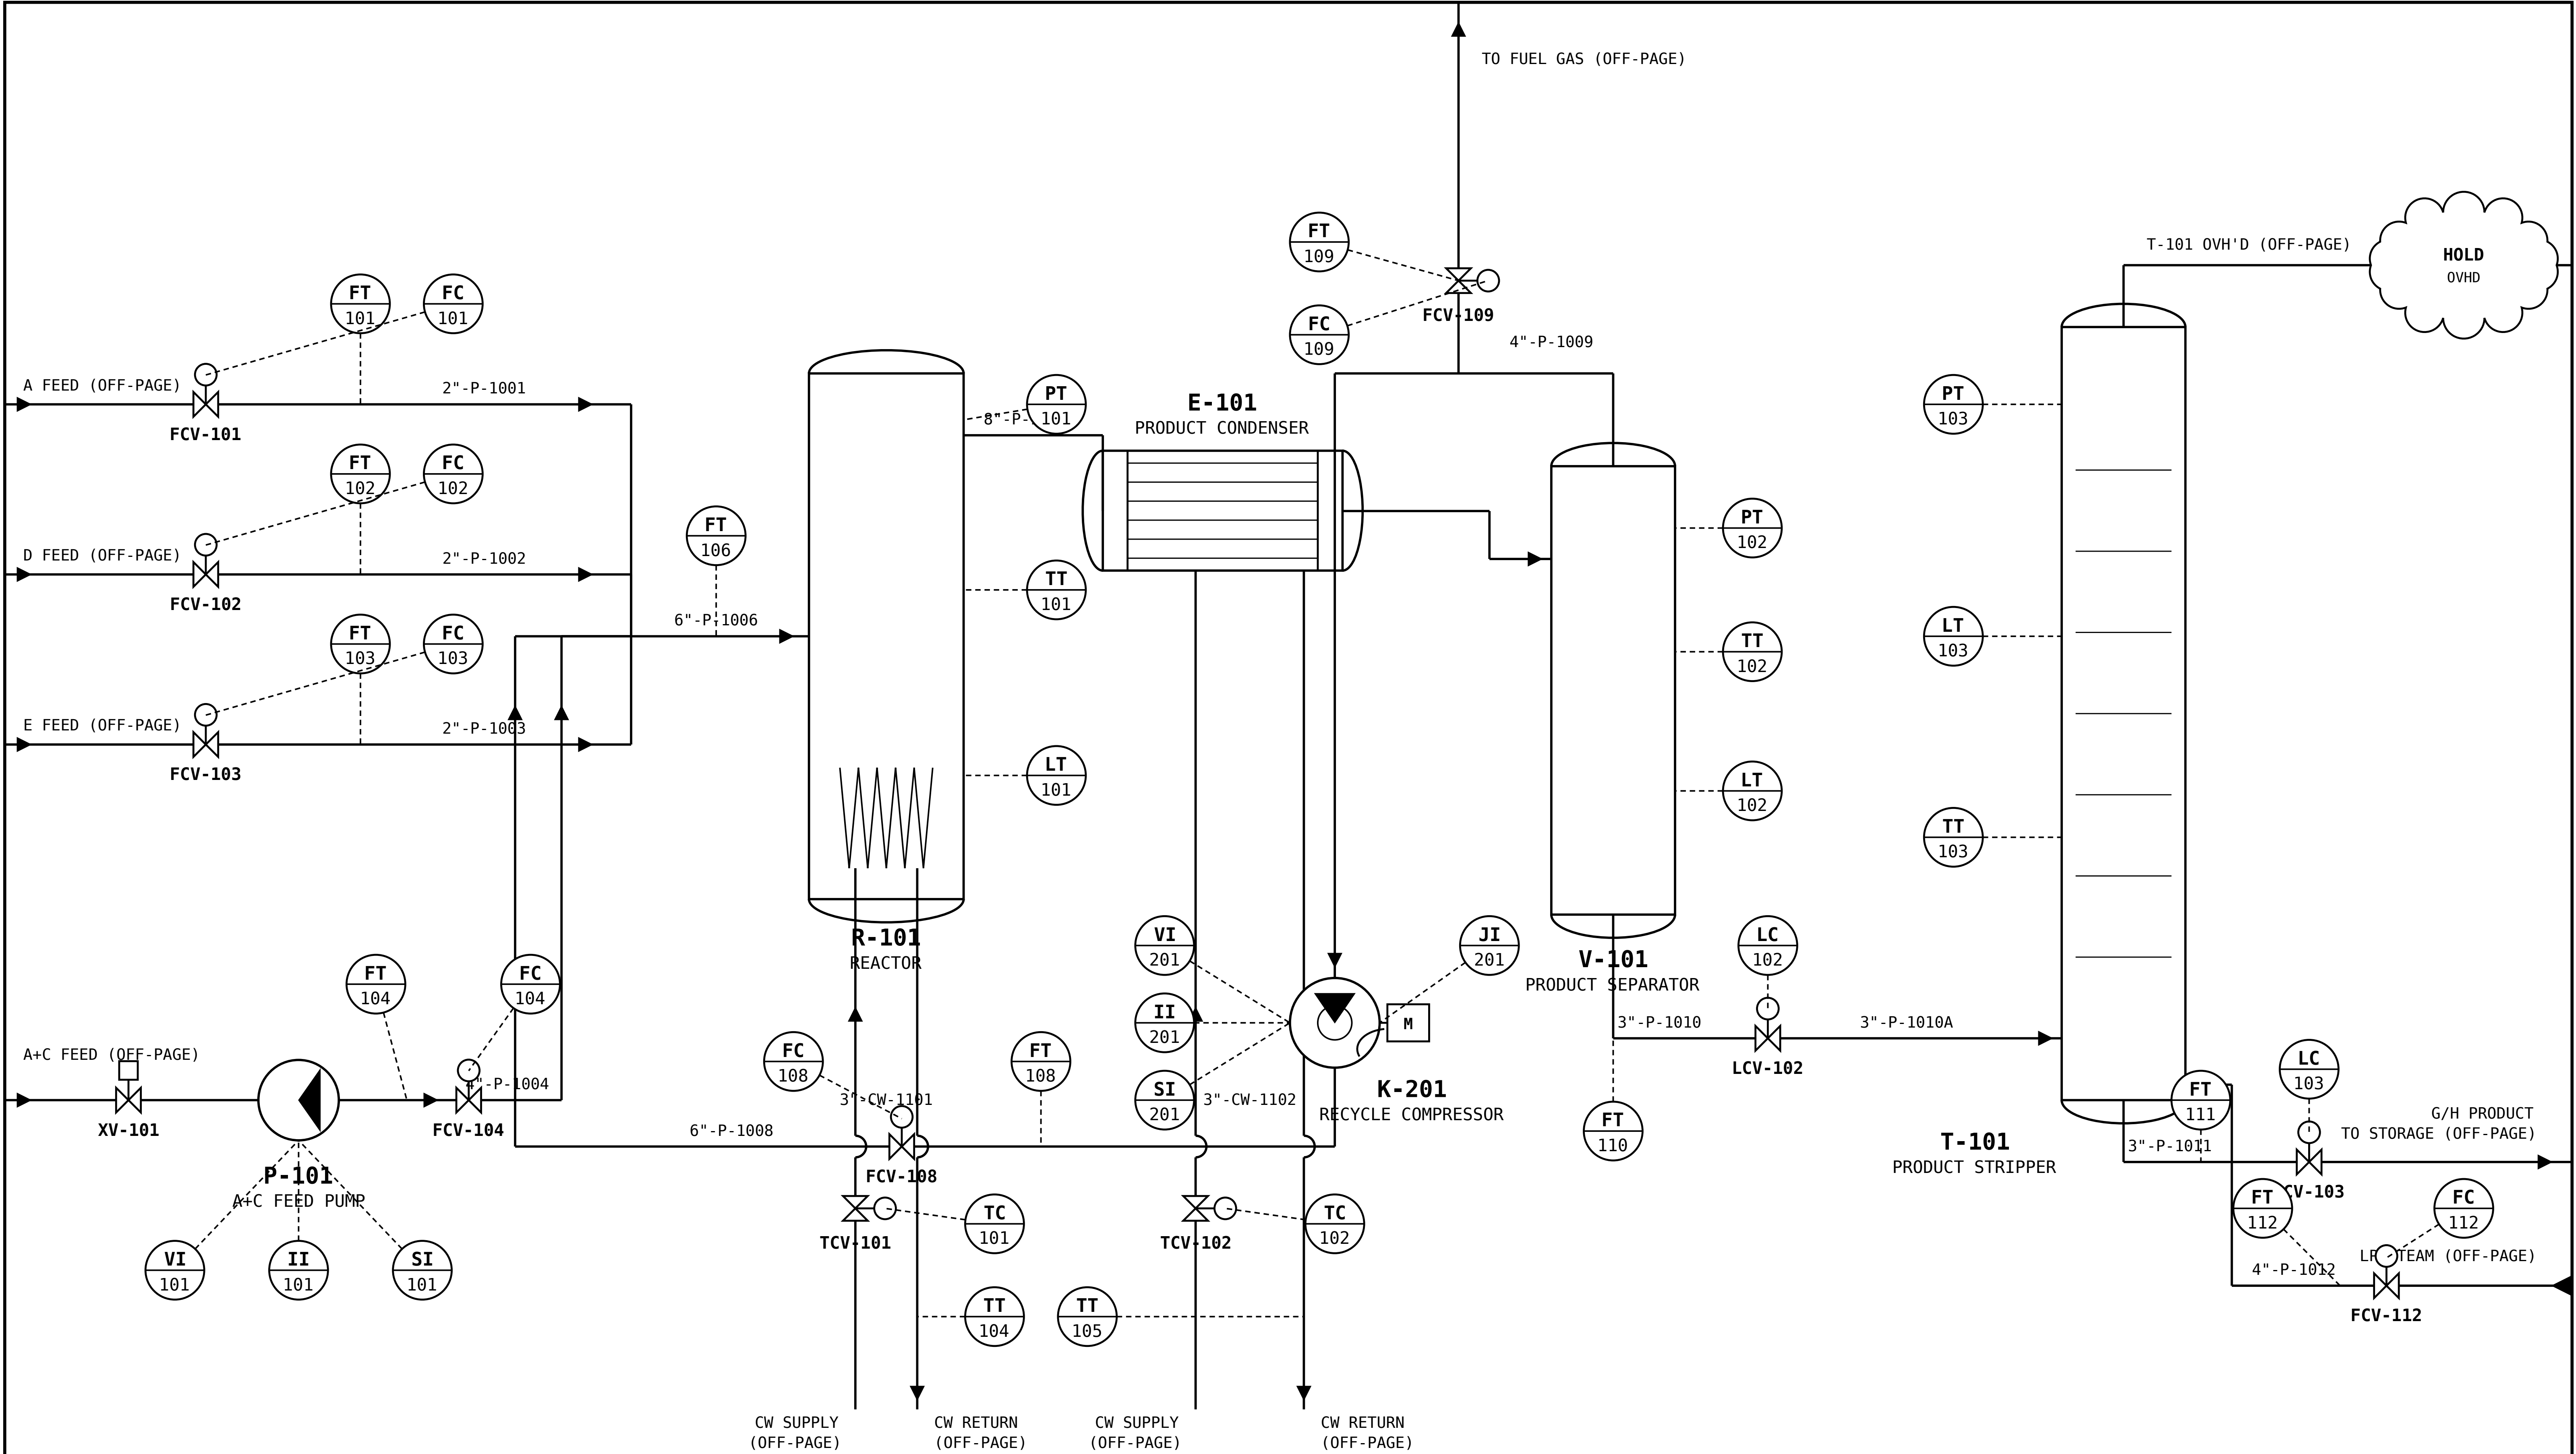

NOTES:

- 1. ANALYZERS AT-201..AT-219 (L0 xmeas_23..xmeas_41) OFF-SHEET.
- 2. L0 JOIN: data/tag_schedule.parquet (tep 180 s; iiot 1 s).
- 3. HOLD CLOUD = OPEN ITEM AT REV B (T-101 OVERHEAD).
- 4. SHEET DRAWN FROM models/unit100_dexpi.json (pyDEXPI).

LAGOS SPECIALTY CHEMICALS		
UNIT 100 – TENNESSEE EASTMAN PROCESS		
PIPING & INSTRUMENTATION DIAGRAM		
DWG LSC-U100-PID-001	REV B	2026-08-18
SCALE: NTS SIZE: ANSI-D SHEET 1 OF 1		